


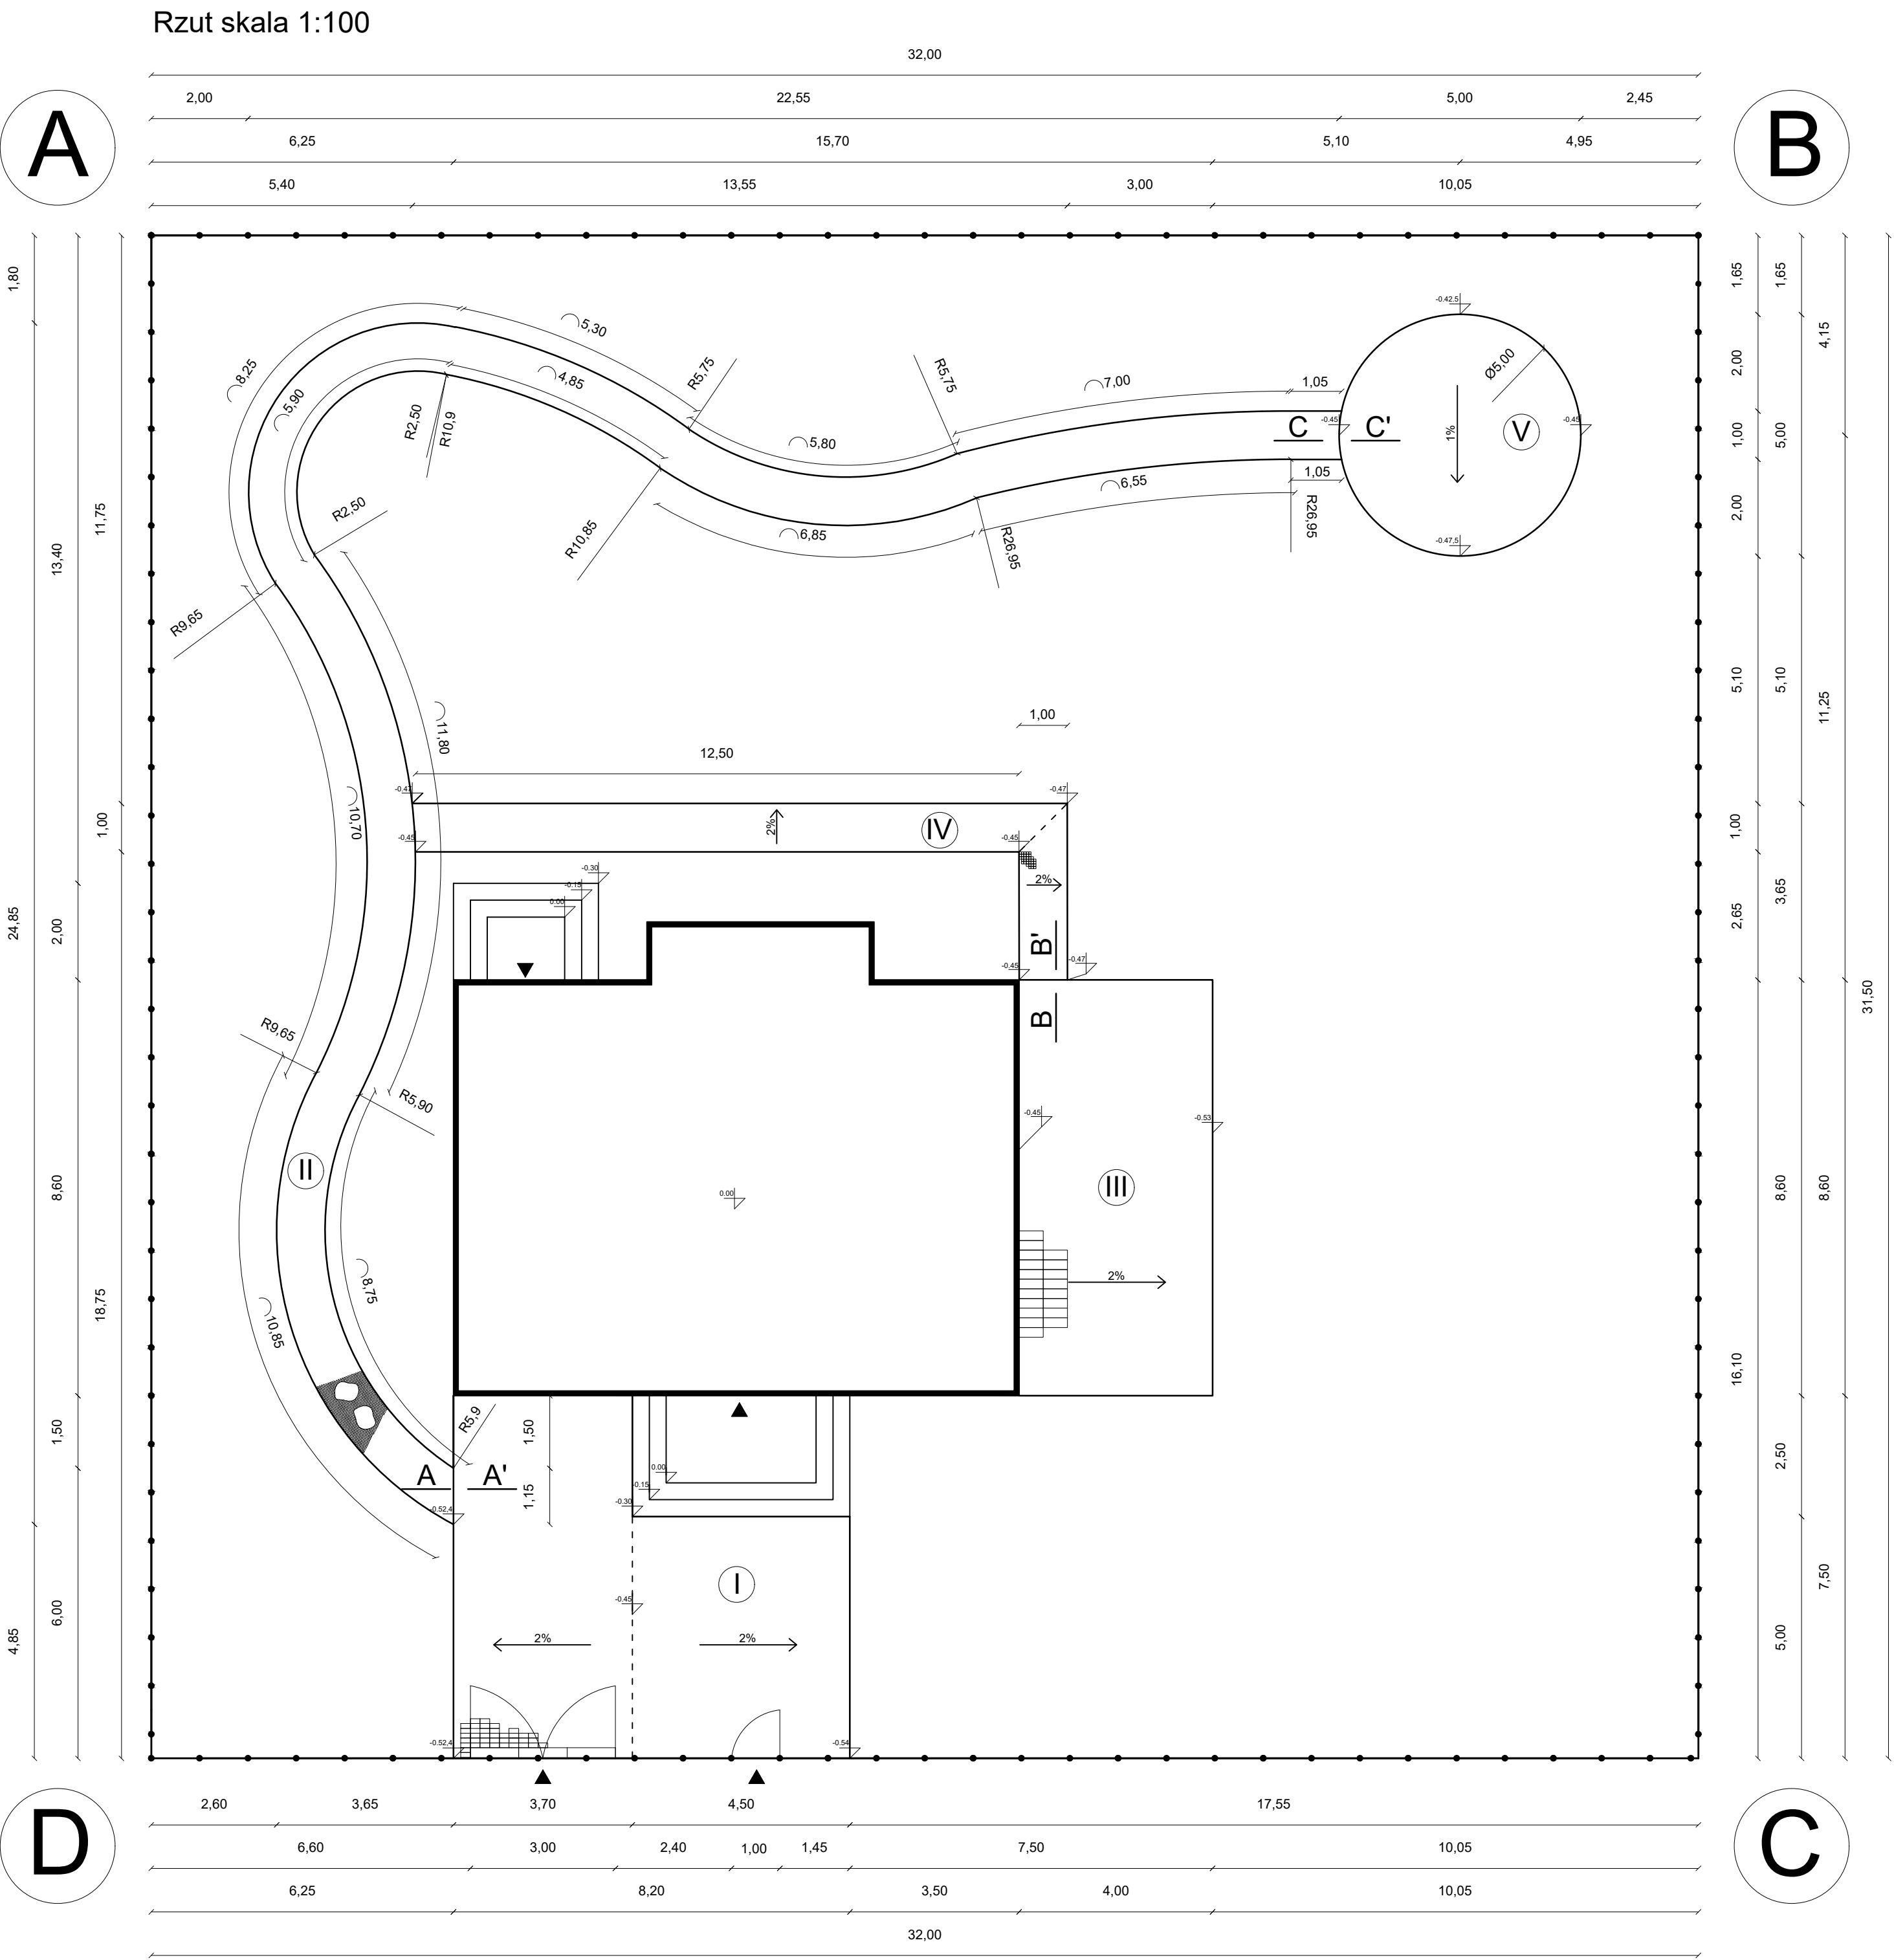


Legenda:


- I droga pieszo-jezdna o nawierzchni z kostki brukowej betonowej z obrzeżami betonowymi, pow. 50,2 m²
 - II droga piesza spacerowa o nawierzchni z płyt deptakowych Ø 45-60 cm i grysu ogrodowego f. 8-16 mm, szer. 1m
 - III droga piesza o nawierzchni z kostki brukowej betonowej z obrzeżami betonowymi, pow. 34,4 m²
 - IV droga piesza docelowa o nawierzchni z kostki brukowej granitowej z obrzeżami betonowymi, pow. 16,2 m²
 - V nawierzchnia betonowa piesza, pow. 19,4 m²
- 2% nachylenie powierzchni placu
- ▲ oznaczenie wejścia do obiektu
- D narożniki placu
- furka wejściowa na działkę
- brama wjazdowa na działkę
- rzędne wysokościowe placu
- linia przełamania nawierzchni
- ogrodzenie działki
- A A' miejsce przekroju nawierzchni

Tabela - wykaz i specyfikacja materiałów budowlanych				
Lp.	Rodzaj materiału budowlanego	Jednostka	Ilość/ nakład	Producent/ norma
1	Krawężnik wjazdowy betonowy 100 x 22 x 20 cm	szt.	3	Polbruk
2	Ława fundamentowa betonowa kl. C12/15	m ³	-	-
3	Obrzeże betonowe 50 x 20 x 5 cm	szt.	124	Firma Maja
4	Kostka brukowa betonowa 20 x 10 x 4 cm	m ²	50,2	Polbruk
5	Płyta deptakowa nieregularna Ø45-60cm piasek pustyni	szt.	50	Bruk-bet
6	Grys ogrodowy Golden Royal f. 8-16 mm	m ³	2	-
7	Kostka brukowa betonowa Triada 50 x 20 x 6 cm	m ²	34,4	Polbruk
8	Kostka brukowa granitowa łupana 5 x 5 x 5 cm	m ²	16,2	Strzegom
9	Nawierzchnia betonowa - beton klasy C25/30	m ³	2,95	Baumit
10	Kostka granitowa płomieniowana 10 x 10 x 10 cm	szt.	20	G602
11	Piasek płukany f. 0-2 mm	m ³	8,85	PN-EN 13043
12	Żwir f. 8-16 mm	m ³	11,2	KAMAR
13	Tłuczeń f. 31,5-63 mm	m ³	23	-
14	Pospółka f. 0-16 mm	m ³	10,5	Fetra


Przekrój A - A' łączenie drogi pieszo-jezdnej o nawierzchni z kostki brukowej betonowej z obrzeżami betonowymi (I) i drogi pieszej spacerowej o nawierzchni z płyt deptakowych i grysu ogrodowego (II), skala 1:10

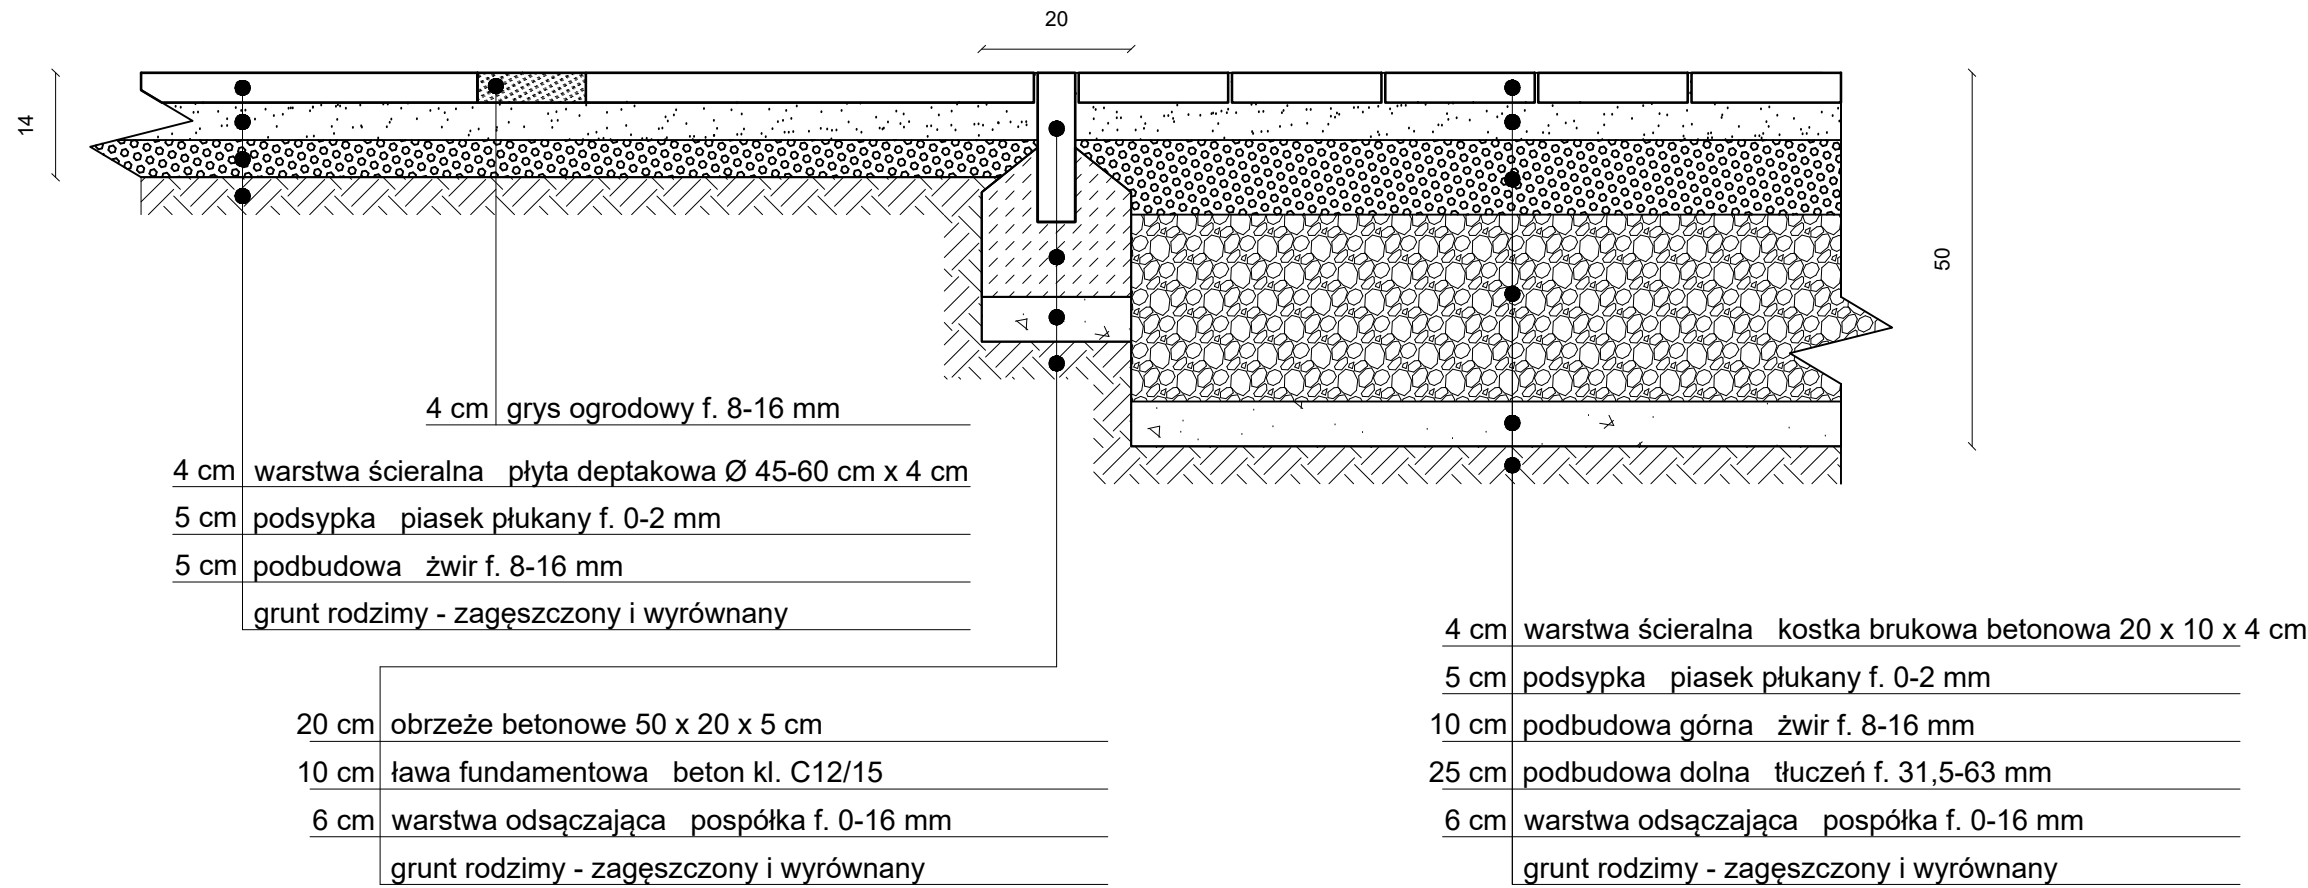

Przekrój B - B' łączenie drogi pieszej o nawierzchni z kostki brukowej betonowej z obrzeżami betonowymi (III) i drogi pieszej docelowej o nawierzchni z kostki brukowej granitowej z obrzeżami betonowymi (IV), skala 1:10

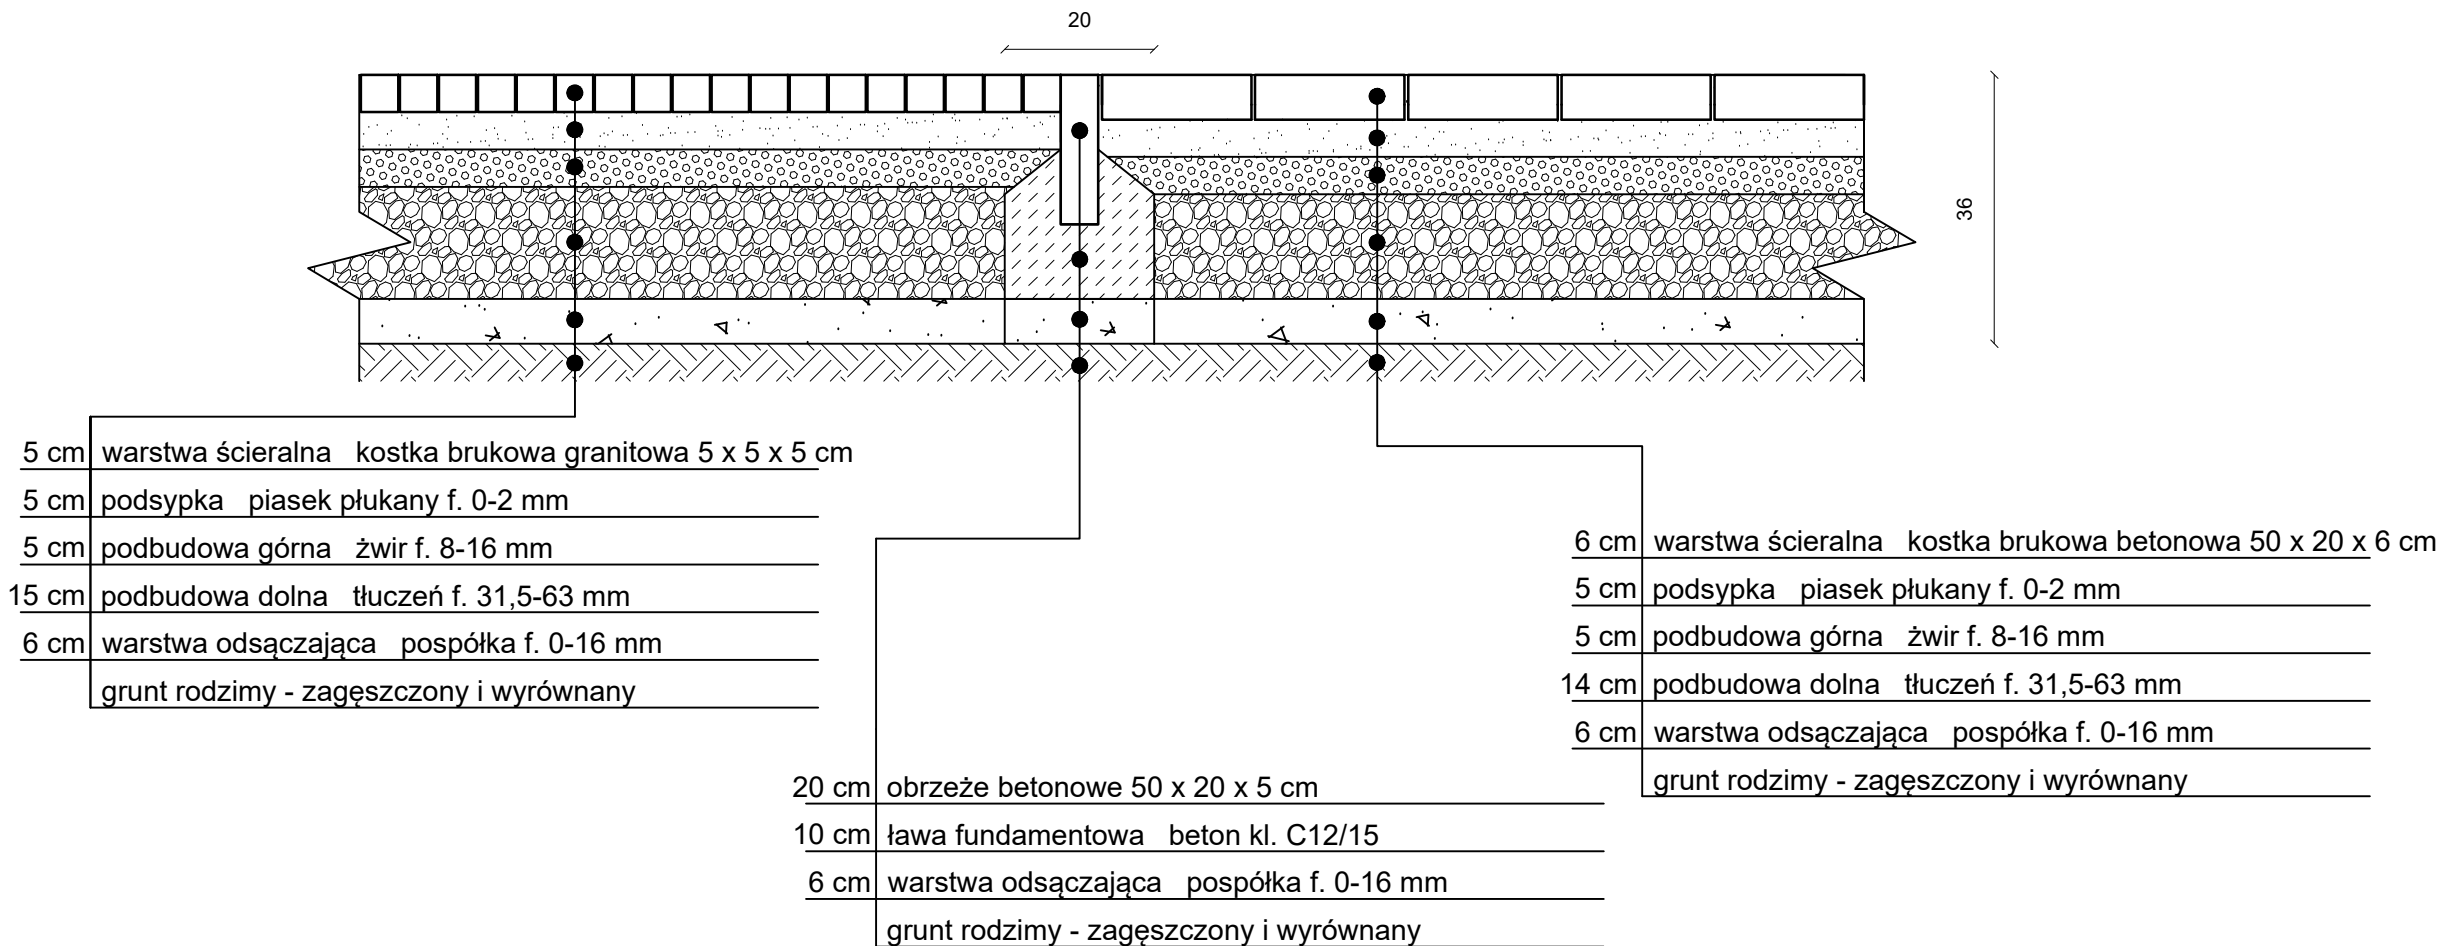

Przekrój C - C' łączenie drogi pieszej spacerowej o nawierzchni z płyt deptakowych i grysu ogrodowego (II) i nawierzchni betonowej pieszej (V), skala 1:10

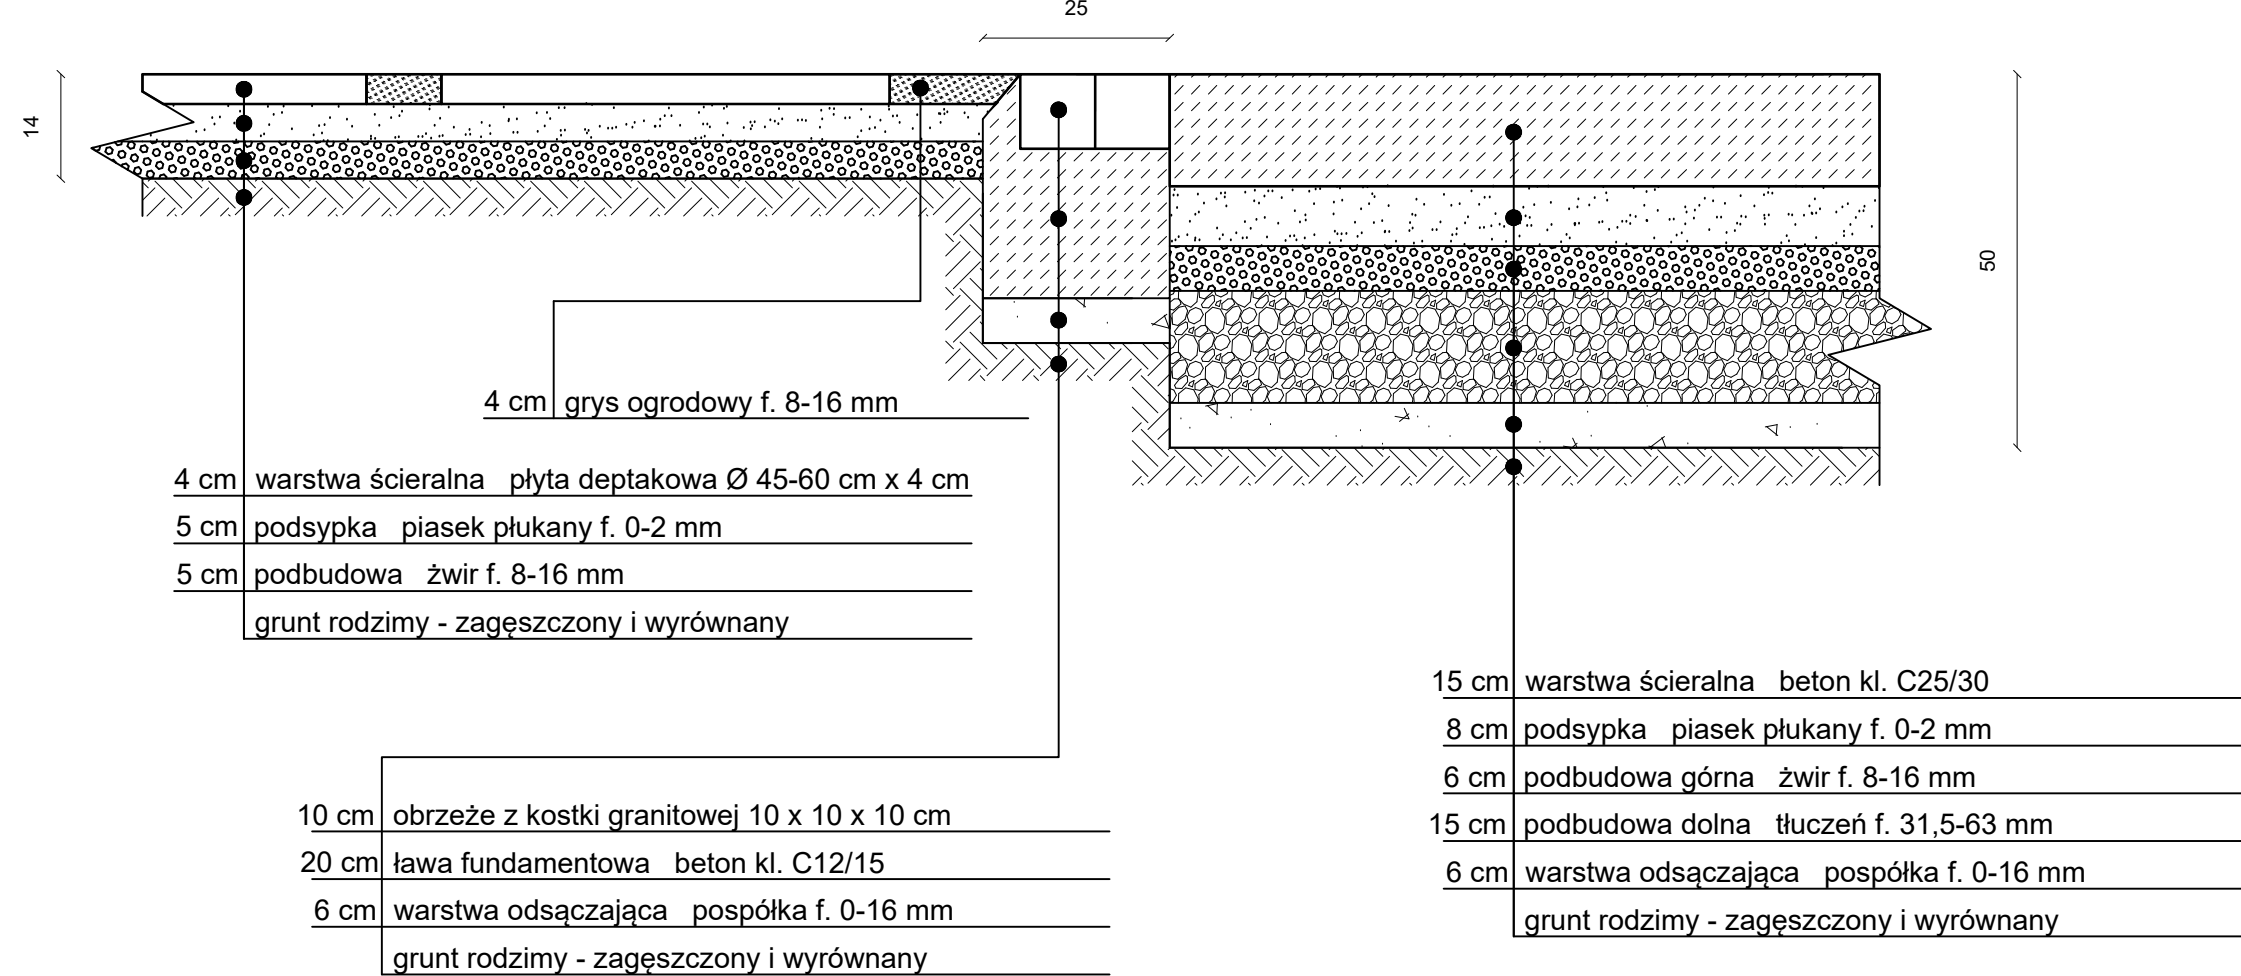

Kierunek: Architektura krajobrazu WBiŚ SGGW Rok II, sem. 4, rok akad. 2025/2026 Przedmiot: Budowa obiektów architektury krajobrazu 2		Temat: projekt wykonawczy nawierzchni Branża: architektura krajobrazu / drogownictwo Etap: projekt dróg i nawierzchni Arkusz 1: Rzut i przekroje nawierzchni	
Wykonał: Paweł Nowak		Sprawdził:	
Skala 1:100 i 1:10	Data:	Ocena:	Uwagi: